


ΕΘΝΙΚΟ ΚΤΗΜΑΤΟΛΟΓΙΟ

ΠΕΡΙΦΕΡΕΙΑΚΗ ΕΝΟΤΗΤΑ : ΦΩΚΙΔΑΣ
ΔΗΜΟΣ : ΔΕΛΦΩΝ
ΔΗΜΟΤΙΚΗ ΕΝΟΤΗΤΑ : ΔΕΛΦΩΝ
ΔΗΜΟΤΙΚΗ ΚΟΙΝΟΤΗΤΑ : ΔΕΛΦΩΝ



ΚΩΔΙΚΟΣ ΑΡΙΘΜΟΣ ΕΘΝΙΚΟΥ ΚΤΗΜΑΤΟΛΟΓΙΟΥ: 480190903113

ΑΠΟΣΠΑΣΜΑ ΚΤΗΜΑΤΟΛΟΓΙΚΟΥ ΔΙΑΓΡΑΜΜΑΤΟΣ ΑΝΑΡΤΗΣΗΣ

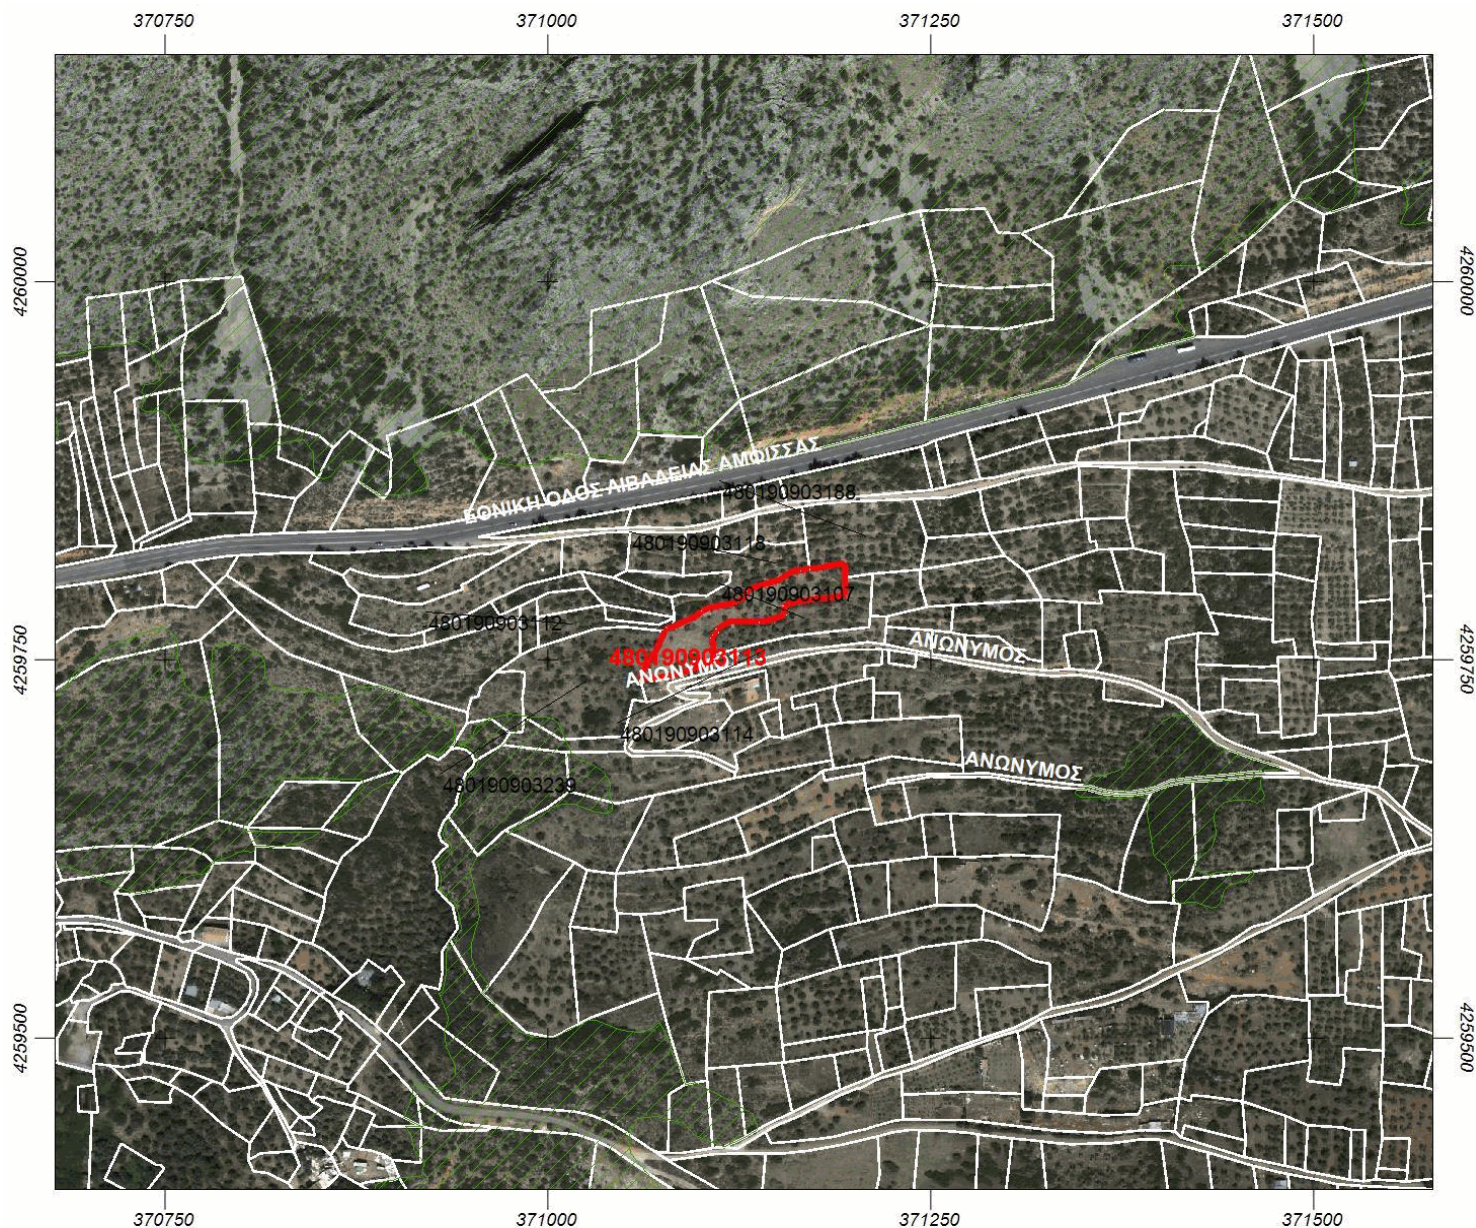

0 25 50 100 150 200 250m

ΚΛΙΜΑΚΑ 1 : 5000

ΥΠΟΜΝΗΜΑ

- Όριο γεωτεμαχίου που αφορά το απόσπασμα
- Όριο γεωτεμαχίου
- - - Όριο χώρου αποκλειστικής χρήσης διηρημένων ιδιοκτησιών
- ▨ Ζώνη δουλείας
- ▨ Διεκδικούμενη δασική έκταση
- Όριο νομής από αναδασμό

Φωτοληψία: 2007 έως 2009

Εμβαδόν γεωτεμαχίου από κτηματογράφηση: 3024 τ.μ.
Εμβαδόν Δήλωσης/Τίτλου: 3.024,12 τ.μ.

Αποδεκτή απόκλιση εμβαδού: $\pm 211,69$ τ.μ.

Σύστημα Αναφοράς: Ε.Γ.Σ.Α. '87

ΕΘΝΙΚΟ ΚΤΗΜΑΤΟΛΟΓΙΟ

ΟΜΟΡΟΙ ΙΔΙΟΚΤΗΤΕΣ ΤΟΥ ΓΕΩΤΕΜΑΧΙΟΥ ΜΕ ΚΑΕΚ: 480190903113

ΚΑΕΚ ΟΜΟΡΟΥ ΓΕΩΤΕΜΑΧΙΟΥ	ΟΝΟΜΑΤΕΠΩΝΥΜΟ ΙΔΙΟΚΤΗΤΗ
480190903114	ΓΟΥΛΙΑΜΟΥ ΓΕΩΡΓΙΑ
480190903239	ΔΑΤΣΙΟΣ ΔΗΜΗΤΡΙΟΣ
480190903239	ΔΑΤΣΙΟΥ ΦΩΤΕΙΝΗ
480190903239	ΖΟΡΜΠΑ ΑΛΕΞΑΝΔΡΑ
480190903239	ΤΣΕΛΙΟΥ ΡΟΖΑΝΑ
480190903239	ΤΣΕΜΠΕΡΟΥΛΗΣ ΔΗΜΗΤΡΙΟΣ
480190903239	ΤΣΕΜΠΕΡΟΥΛΗΣ ΠΑΝΑΓΙΩΤΗΣ

ΕΘΝΙΚΟ ΚΤΗΜΑΤΟΛΟΓΙΟ

ΣΥΝΤΕΤΑΓΜΕΝΕΣ ΚΟΡΥΦΩΝ ΓΕΩΤΕΜΑΧΙΟΥ ΜΕ ΚΑΕΚ: 480190903113

<u>ΑΑ</u>	Συντεταγμένες κορυφών του γεωτεμαχίου	
	<u>Χ</u>	<u>Υ</u>
1	371081.550	4259771.410
2	371092.870	4259776.500
3	371097.550	4259778.710
4	371100.460	4259781.790
5	371105.060	4259783.730
6	371121.840	4259787.320
7	371123.780	4259788.530
8	371125.710	4259789.080
9	371129.810	4259792.060
10	371130.490	4259794.920
11	371133.830	4259797.160
12	371146.990	4259801.340
13	371151.250	4259802.350
14	371159.550	4259807.700
15	371161.500	4259808.140
16	371165.470	4259808.700
17	371169.590	4259809.450
18	371171.341	4259809.723
19	371180.680	4259811.180
20	371183.270	4259811.520
21	371187.030	4259812.510
22	371194.470	4259812.680
23	371194.386	4259804.042
24	371194.350	4259800.350
25	371194.280	4259792.460
26	371183.500	4259790.700
27	371174.620	4259789.790
28	371161.930	4259787.580
29	371153.940	4259784.950
30	371155.470	4259779.260
31	371145.580	4259775.660
32	371138.620	4259774.370
33	371133.940	4259774.620
34	371127.010	4259774.440
35	371118.820	4259774.360

ΕΘΝΙΚΟ ΚΤΗΜΑΤΟΛΟΓΙΟ

36	371115.260	4259772.550
37	371112.590	4259771.550
38	371110.480	4259770.140
39	371111.550	4259767.750
40	371107.710	4259765.800
41	371107.260	4259763.740
42	371107.670	4259759.790
43	371108.483	4259752.993
44	371108.860	4259749.840
45	371108.200	4259748.790
46	371098.830	4259744.780
47	371094.790	4259743.650
48	371082.390	4259739.870
49	371070.800	4259737.680
50	371065.840	4259737.260
51	371061.710	4259737.490
52	371061.780	4259739.230
53	371063.010	4259743.040
54	371066.250	4259748.460
55	371070.140	4259753.850
56	371076.600	4259768.530
57	371078.110	4259770.770
58	371081.550	4259771.410

Παρατηρήσεις

1. Η ακρίβεια των συντεταγμένων είναι αυτή που ορίζεται από τις τεχνικές προδιαγραφές του Εθνικού Κτηματολογίου, με τις οποίες συντάχθηκαν τα κτηματολογικά διαγράμματα.
2. Το πλήθος των δεκαδικών ψηφίων στις συντεταγμένες δεν υποδηλώνει την ακρίβεια τους, αλλά δίνεται ώστε να ελαχιστοποιηθεί τυχόν σφάλμα στρογγύλευσης στον υπολογισμό του εμβαδού.
3. Η κλίμακα απόδοσης του διαγράμματος εξυπηρετεί την ευκρίνεια του σχεδίου και δεν αντιστοιχεί απαραίτητα στην ακρίβεια συλλογής των δεδομένων.